


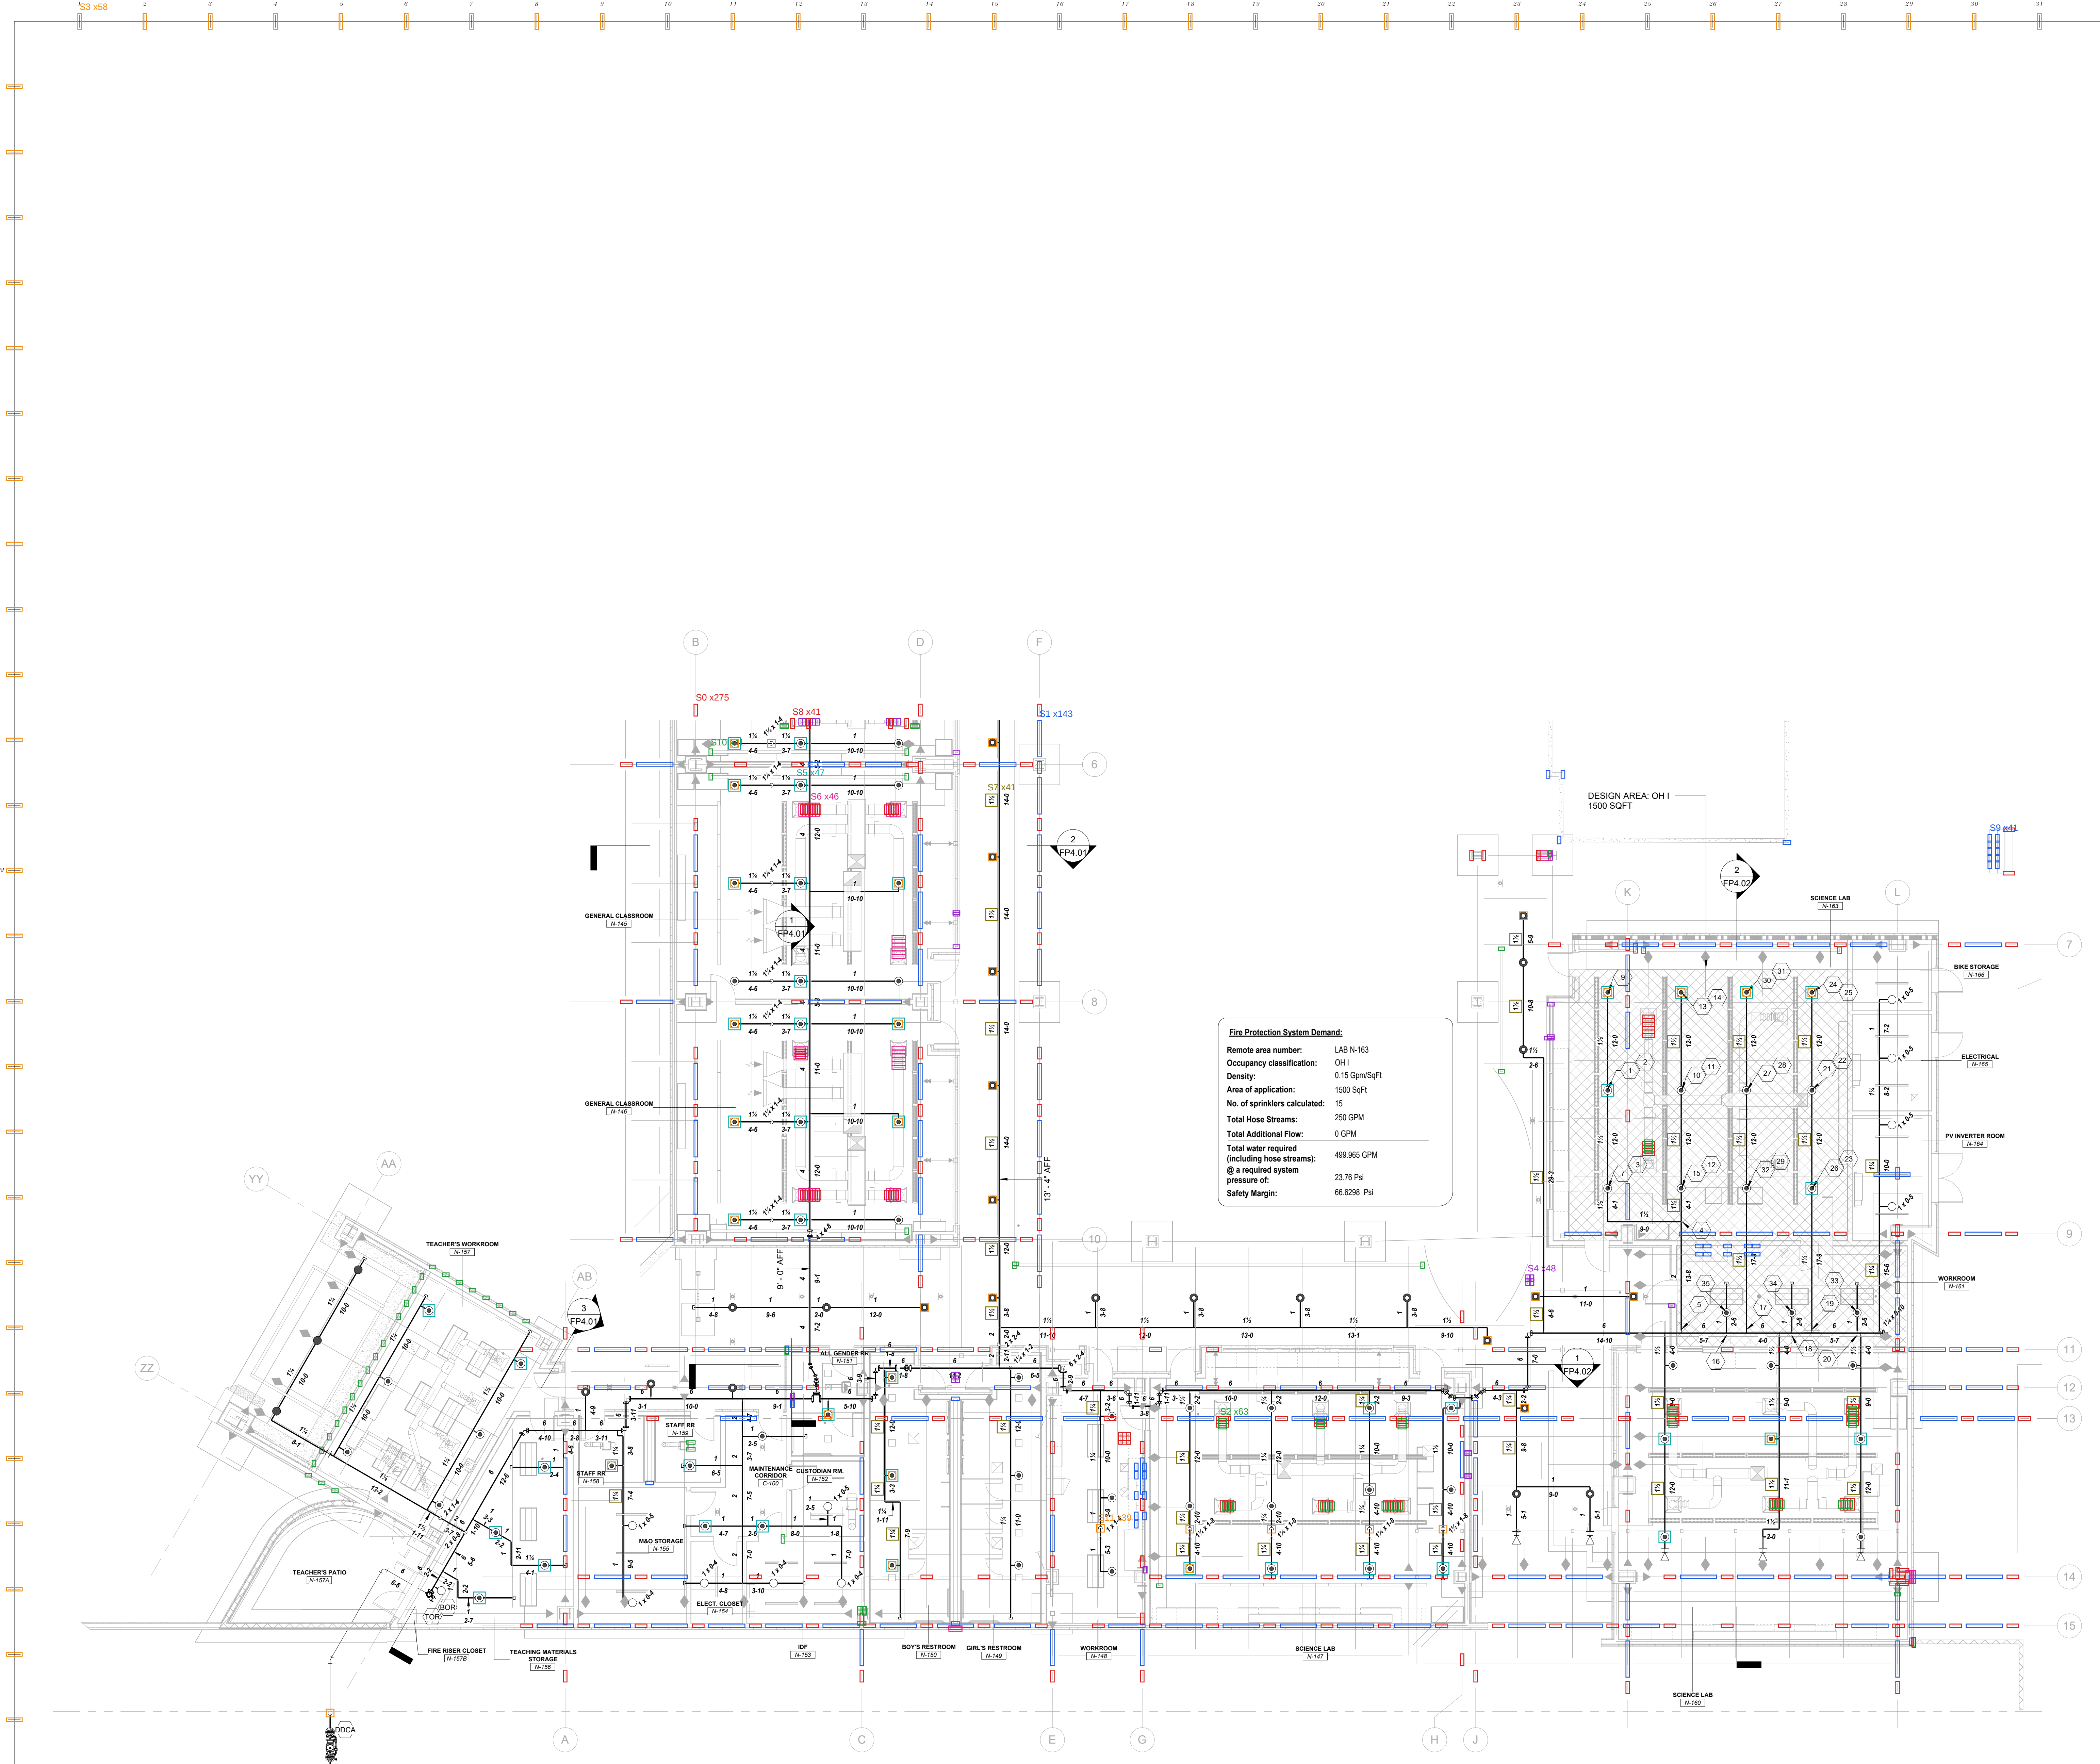

FIRE PROTECTION ENLARGED FLOOR PLAN - EAST

SCALE
1/8" = 1'-0"

1

PROJECT TYPE		DRAWING PHASE SCHEDULE							
D&A SUBMITTAL	NON-D&A SUBMITTAL	PRELIMINARY SCHEMATIC DESIGN	FINAL SCHEMATIC DESIGN	DESIGN DEVELOPMENT	80% CONSTRUCTION DOCUMENTS	100% CONSTRUCTION DOCUMENTS	D&A APPROVED	BIDDING	CONSTRUCTION
		DEC. 22, 2025	MAR. 10, 2026	JUN. 15, 2026					

DIVISION OF THE STATE ARCHITECT



LOS ANGELES
UNIFIED
SCHOOL DISTRICT
DESIGN & A/E
TECHNICAL SUPPORT
FACILITIES SERVICES DIVISION
333 S. BEAUDRY AVENUE, 23RD
FLOOR
LOS ANGELES, CALIFORNIA 90017

PROJECT TITLE AND SCHOOL LOCATION

JAMES MADISON MIDDLE
SCHOOL CLASSROOM
REPLACEMENT PROJECT

JAMES MADISON
MIDDLE SCHOOL
13000 HART ST.,
NORTH HOLLYWOOD, CA 91605
CAFM SITE ID -13627
MADISON MS LOCATION CODE (R230)

COMMISSIONED ARCHITECT

JOHNSON
FAVARO


JOHNSON FAVARO
Architects and Urban Design
5886 Blackwelder Street
Culver City, CA 90232
(Tel) 310-559-5720
www.johnsonfavaro.com

CONSULTANT

PDS
Pocock Design Solutions Inc.

The drawings and specifications, ideas, designs, and arrangements are and shall remain the property of the architect. No part thereof shall be copied or used in connection with any work or project other than the specific project for which they have been prepared without the written consent of the architect. Visual contact with these drawings or specifications shall constitute evidence of acceptance of these restrictions.
Written dimensions on these drawings shall have precedence over scaled dimensions. Contractor shall verify and be responsible for all dimensions and conditions on the job and this office must be notified of any variation from the dimensions and conditions shown by these drawings. Shop details must be submitted to this office for approval before proceeding with fabrication.
© Johnson Favaro 2025

STAMPS/SEALS

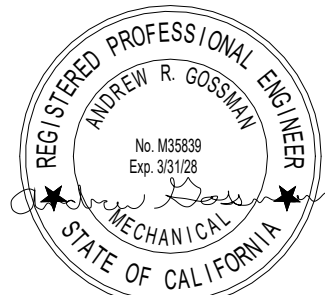

100% DD 06/15/26
100% FINAL SD 03/10/26

SHEET TITLE:

FIRE PROTECTION
ENLARGED FLOOR
PLAN - EAST

CULIN NO.: 10374452 PROJECT ARCH: JF
DRAWN: JF CHECKED: JF
SHEET NUMBER

FP2.20

DATE: SHEET: OF: