


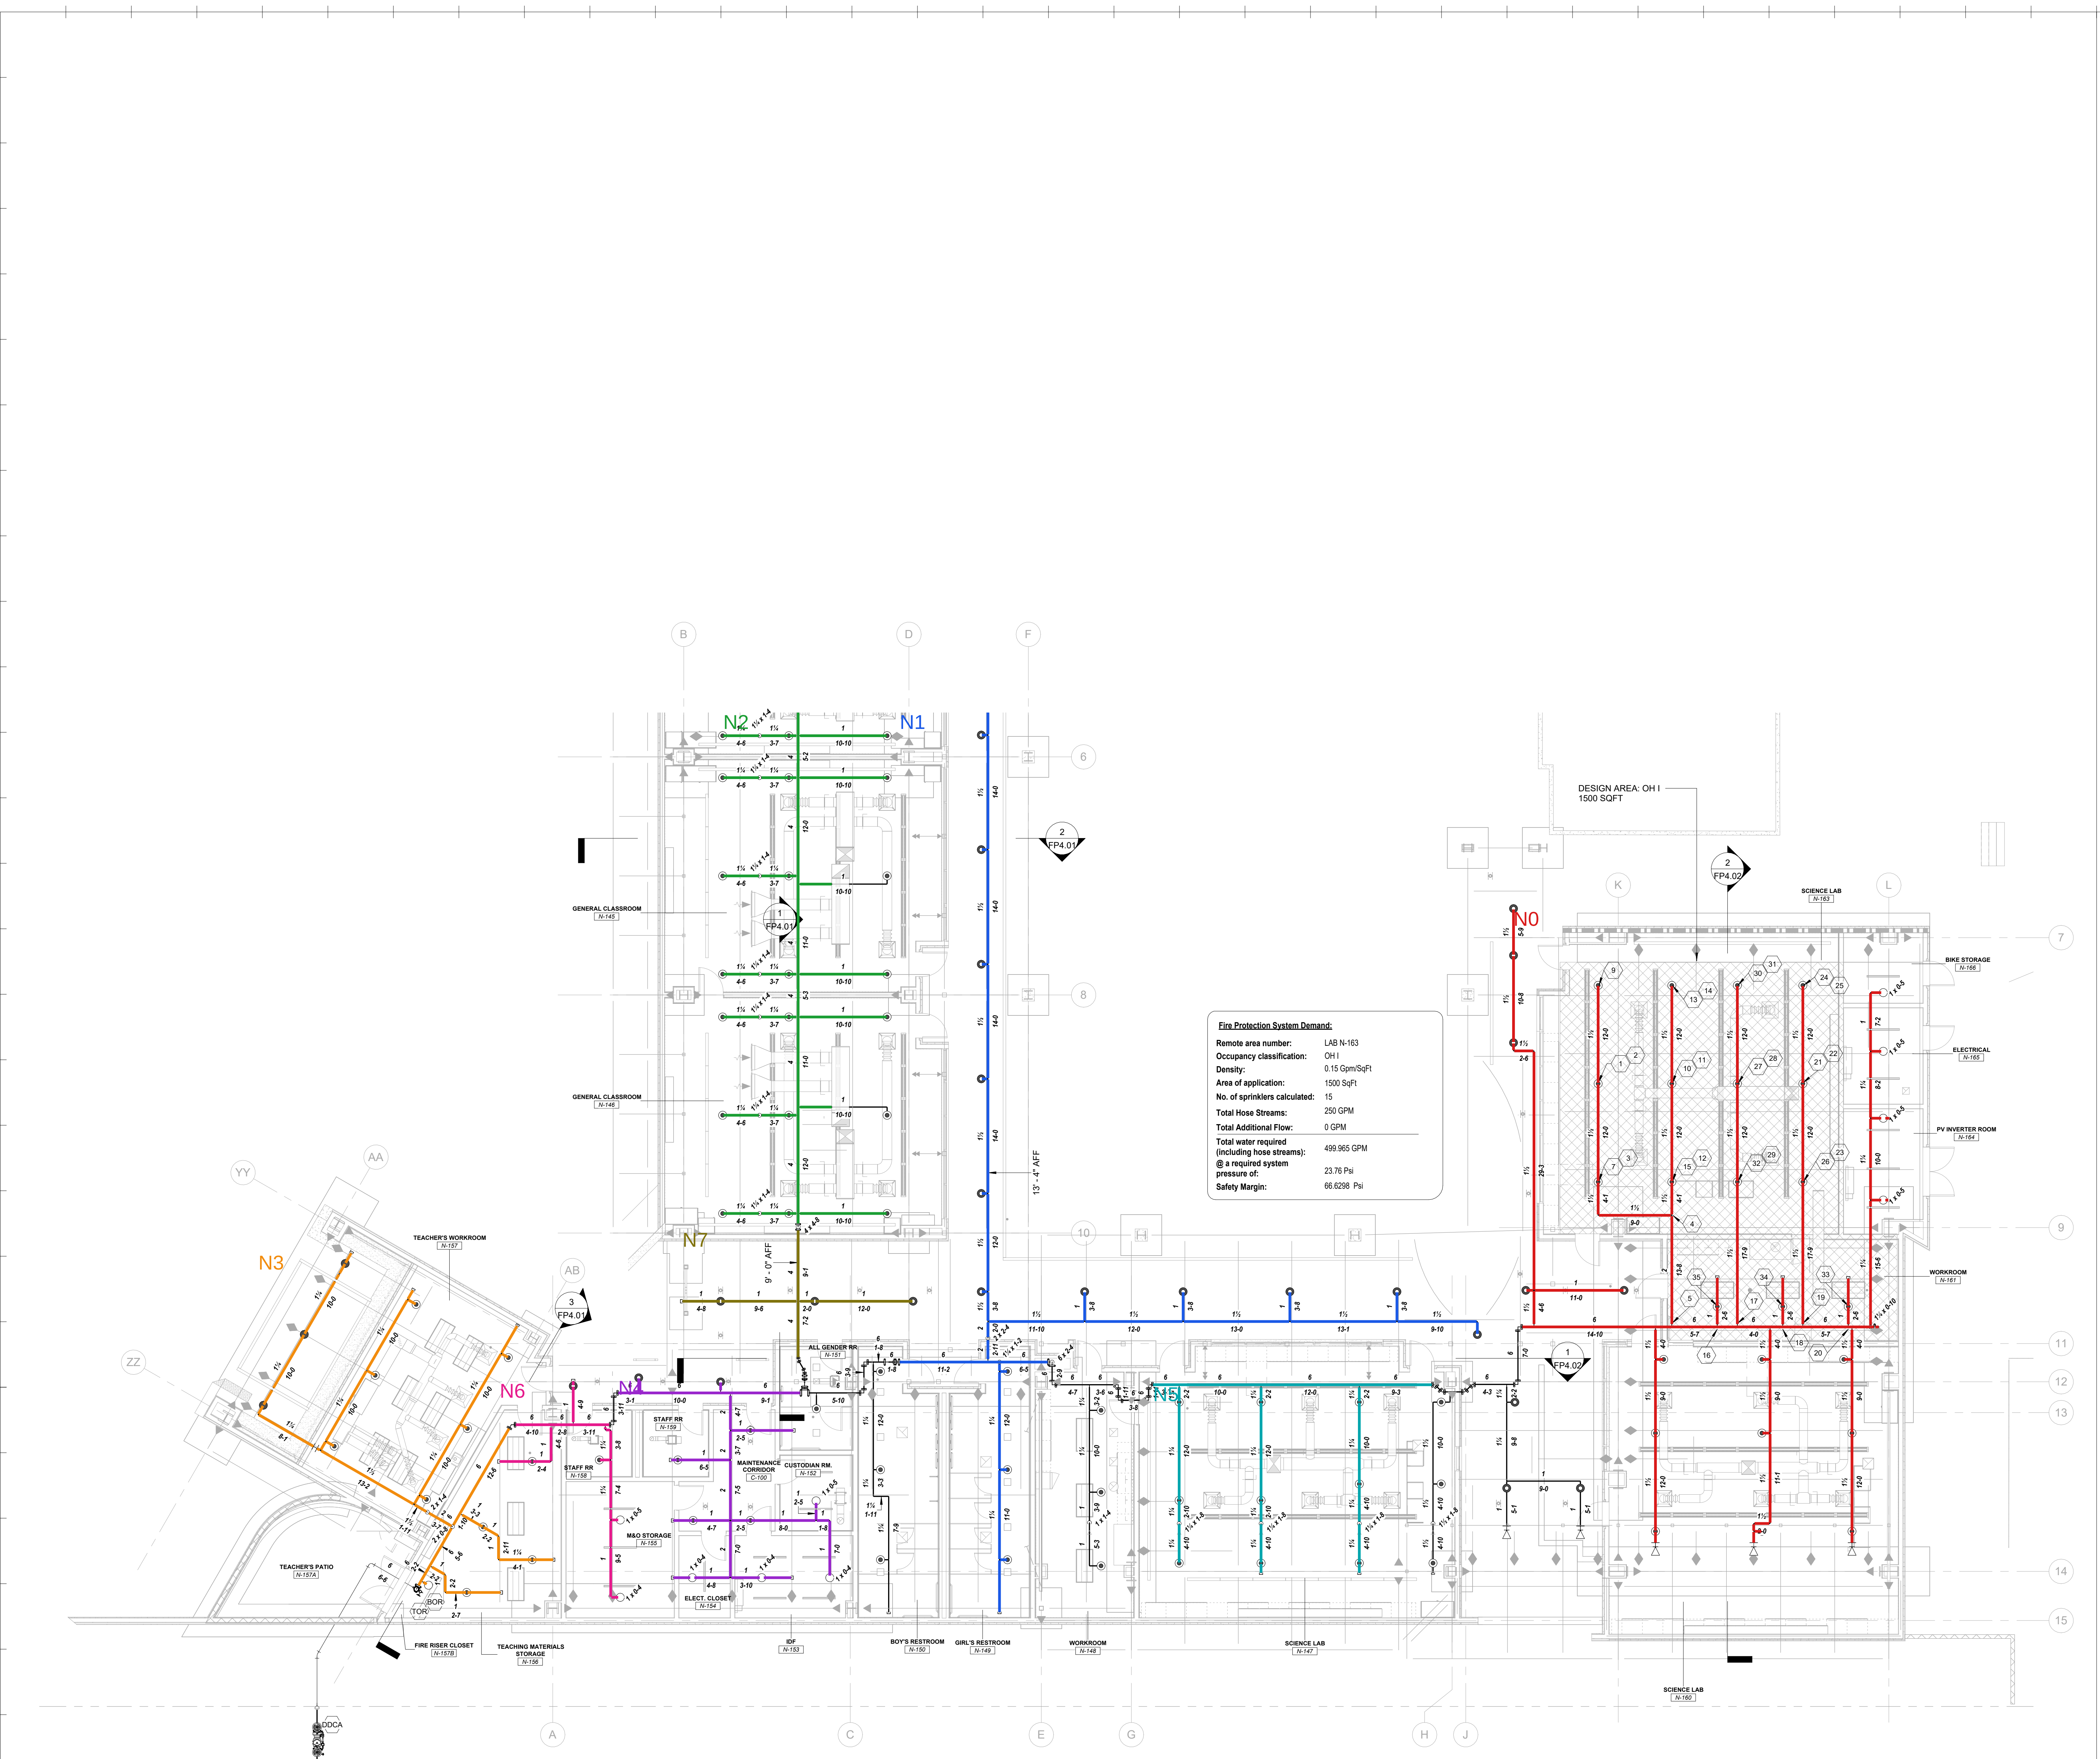

| PROJECT TYPE  |                   | DRAWING PHASE SCHEDULE       |                        |                    |                            |                             |              |         |              |
|---------------|-------------------|------------------------------|------------------------|--------------------|----------------------------|-----------------------------|--------------|---------|--------------|
| DIA SUBMITTAL | NON-DIA SUBMITTAL | PRELIMINARY SCHEMATIC DESIGN | FINAL SCHEMATIC DESIGN | DESIGN DEVELOPMENT | 80% CONSTRUCTION DOCUMENTS | 100% CONSTRUCTION DOCUMENTS | DIA APPROVED | BIDDING | CONSTRUCTION |
|               |                   | DEC. 22, 2025                | MAR. 10, 2026          | JUN. 15, 2026      |                            |                             |              |         |              |

FIRE PROTECTION ENLARGED FLOOR PLAN - EAST

SCALE  
1/8" = 1'-0"

1

DIVISION OF THE STATE ARCHITECT



LOS ANGELES  
UNIFIED  
SCHOOL DISTRICT  
DESIGN & A/E  
TECHNICAL SUPPORT  
FACILITIES SERVICES DIVISION  
333 S. BEAUDRY AVENUE, 23RD  
FLOOR  
LOS ANGELES, CALIFORNIA 90017

PROJECT TITLE AND SCHOOL LOCATION

JAMES MADISON MIDDLE  
SCHOOL CLASSROOM  
REPLACEMENT PROJECT

JAMES MADISON  
MIDDLE SCHOOL  
13000 HART ST.,  
NORTH HOLLYWOOD, CA 91605

CAFM SITE ID -13627  
MADISON MS LOCATION CODE (R230)

COMMISSIONED ARCHITECT

JOHNSON  
FAVARO

JOHNSON FAVARO  
Architects and Urban Design  
5896 Blackwelder Street  
Culver City, CA 90232  
(Tel) 310-559-5720  
www.johnsonfavaro.com

CONSULTANT

PDS  
Pocock Design Solutions Inc.

The drawings and specifications, ideas, designs, and arrangements are and shall remain the property of the architect. No part thereof shall be copied or used in connection with any work or project other than the specific project for which they have been prepared without the written consent of the architect. Visual contact with these drawings or specifications shall constitute evidence of acceptance of these restrictions.

Written dimensions on these drawings shall have precedence over scaled dimensions. Contractor shall verify and be responsible for all dimensions and conditions on the job and this office must be notified of any variation from the dimensions and conditions shown by these drawings. Shop details must be submitted to this office for approval before proceeding with fabrication.

© Johnson Favaro 2025

STAMPS/SEALS



100% DD 06/15/26  
100% FINAL SD 03/10/26

SHEET TITLE:

FIRE PROTECTION  
ENLARGED FLOOR  
PLAN - EAST

COLN NO.: 10374452 PROJECT ARCH: JF  
DRAWN: JF CHECKED: JF  
SHEET NUMBER

FP2.20

DATE: SHEET: OF: